


## 中间模块立面桁架片

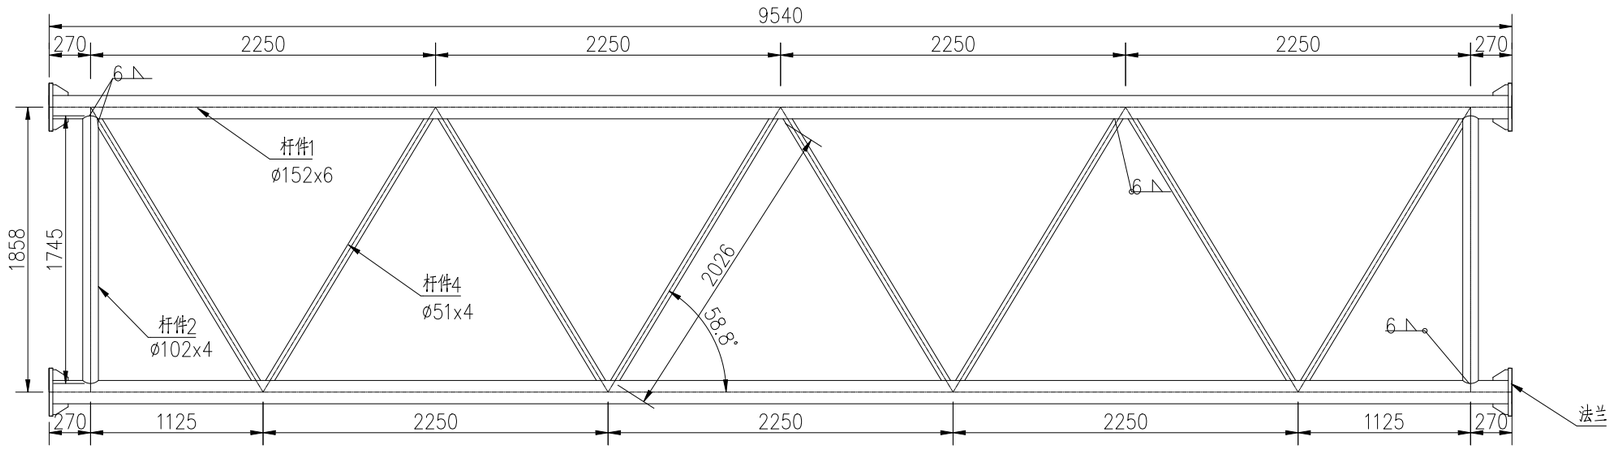


## 桁架横断面图

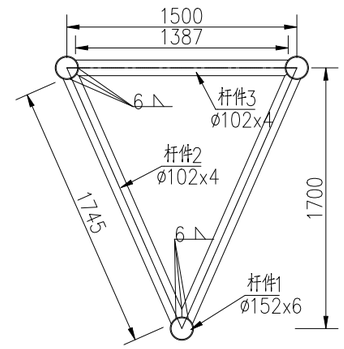


## 中间模块顶面桁架片

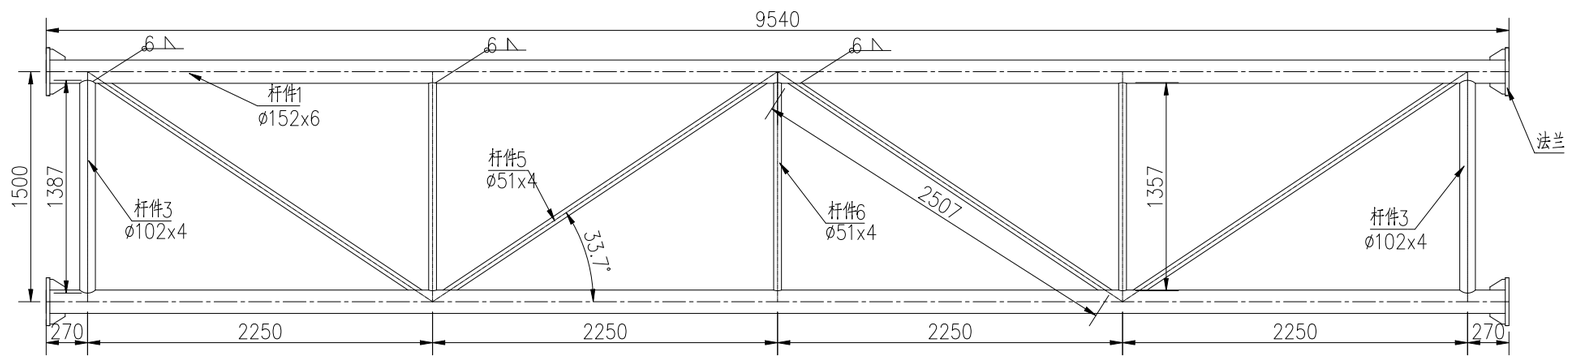


说明：1、本图尺寸除特殊说明外，其余均以mm计；
2、图中未标出类型焊缝焊脚高度均为6mm。

| 中交二公局工程设计研究院 | 张靖皋长江大桥施工暨股权投资项目 ZJG-A7标段 | 横向通道中间模块桁架结构图 | 设计 | | 复核 | | 一审 | | 二审 | | 三审 | | 图号 | MD5-04 | 日期 | 2025.08 |
|---|---|---|---|---|---|---|---|---|---|---|---|---|---|---|---|---|