




横向通道总体布置立面图

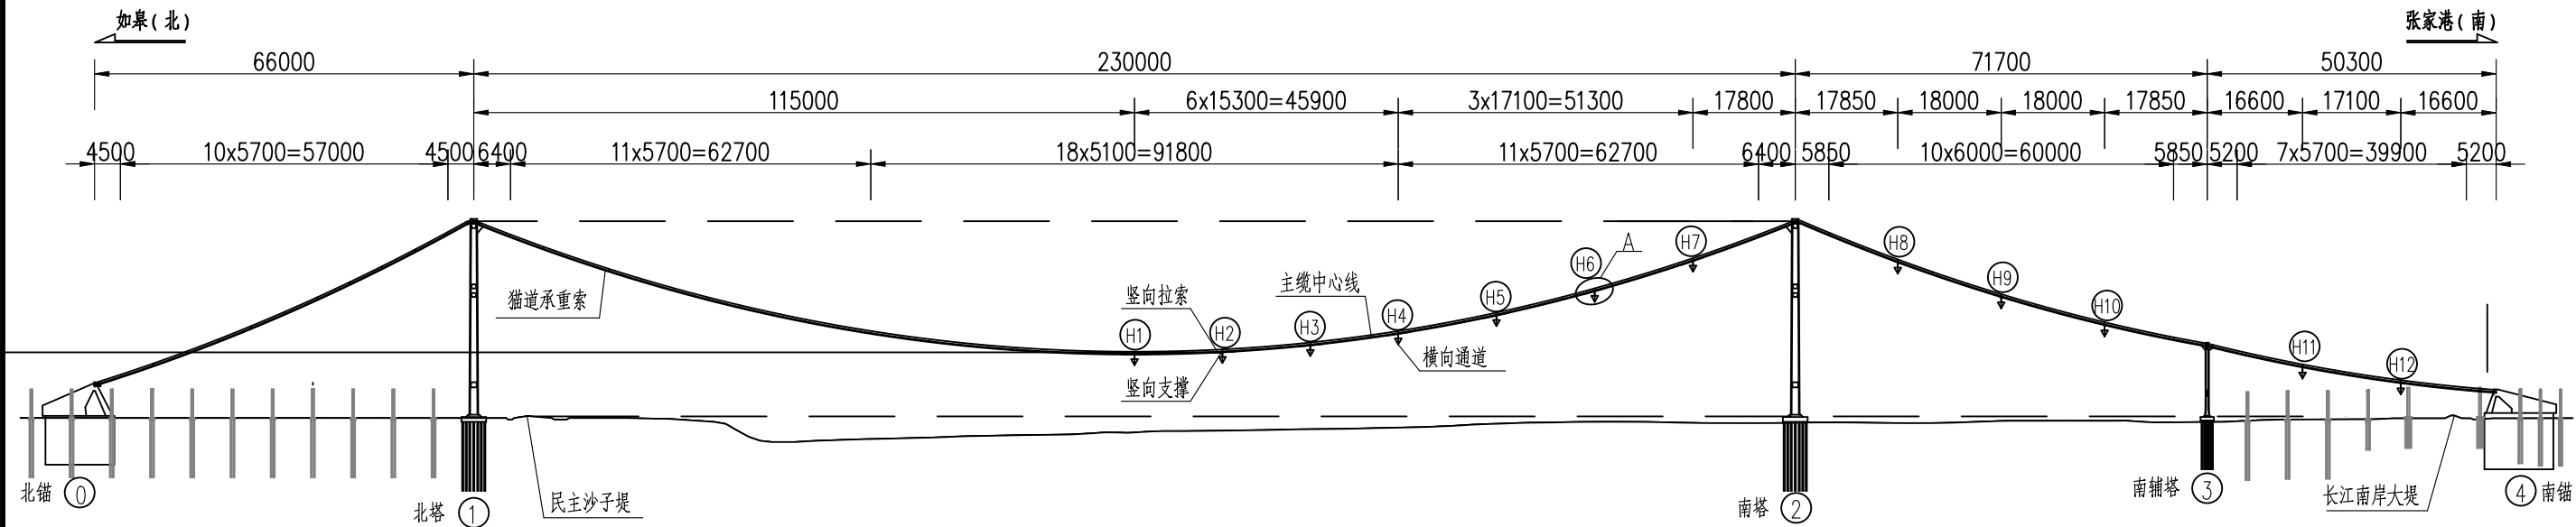


横向通道总体布置平面图

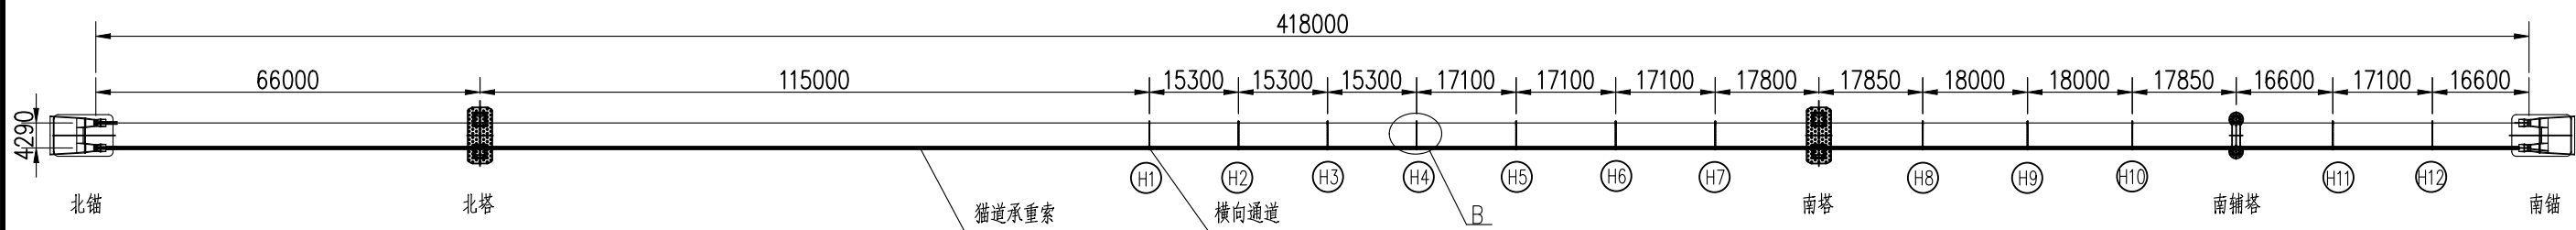

A 局部大样图

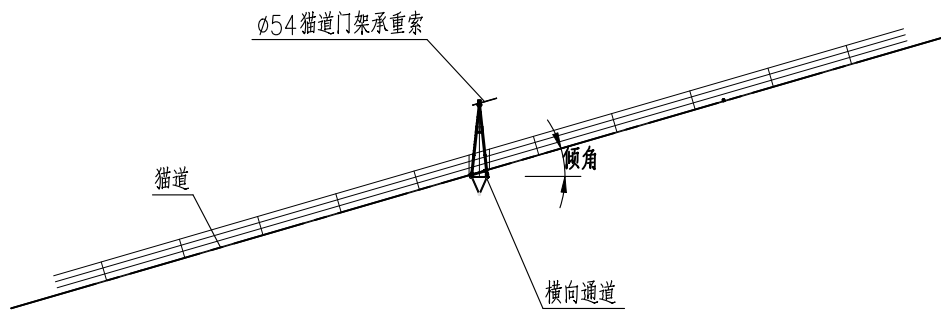

B 局部大样图

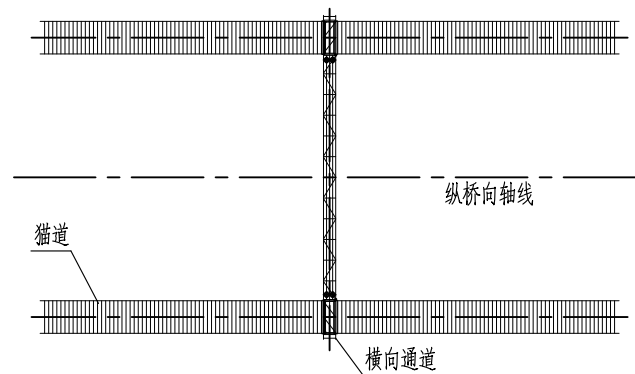

说明：

1. 本图尺寸均以cm计;
2. 本标段包括主跨跨中及其以南横向通道，其中南辅跨(张家港侧)设置3道横向通道，南边跨(张家港侧)设置2道横向通道，主跨跨中及其以南至南主跨设置7道横向通道猫道。
3. 本图适用于张靖皋长江大桥ZJG-A7标段横向通道总体布置图。