“a大样”

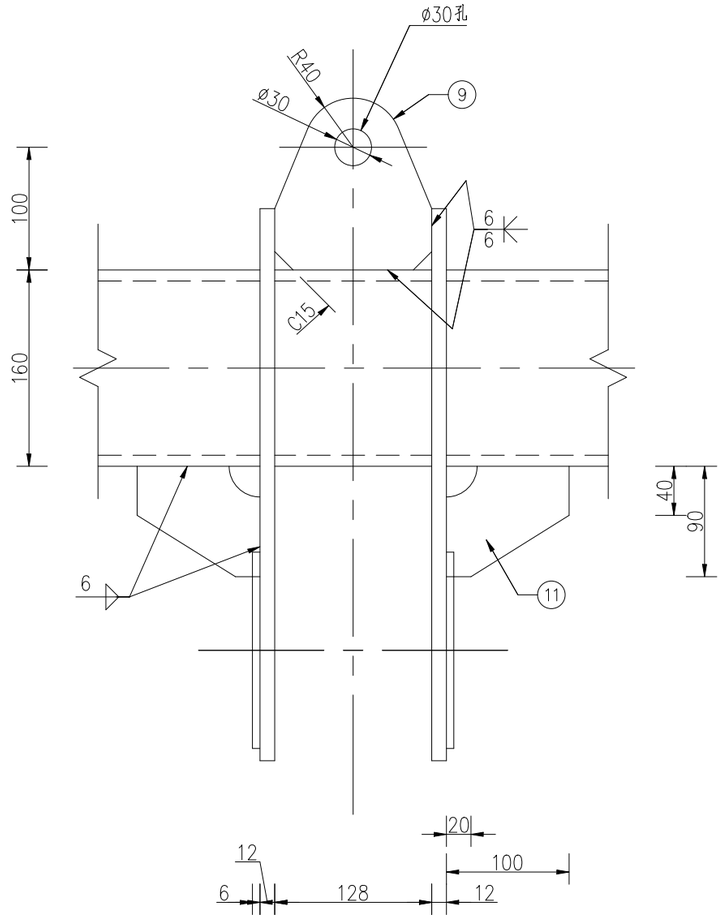

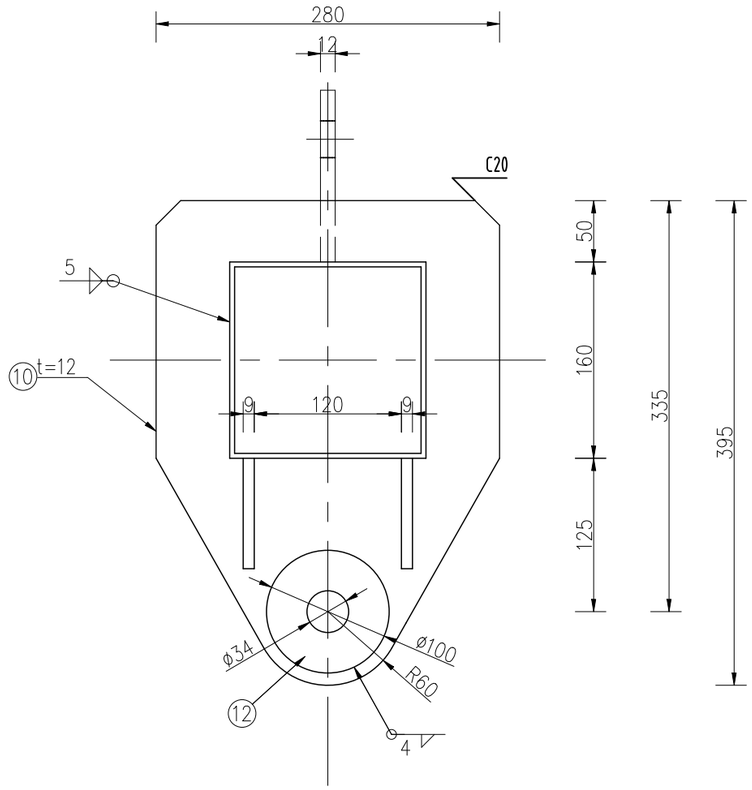

单套材料数量表（单幅共71套）

编号	名称	规格	材质	数量	单重	合计
9	钢板1	140×128×12	Q235	2	1.7	3.4
10	钢板2	395×280×12	Q235	4	8.5	34.0
11	肋板	100×90×9	Q235	8	0.5	3.9
12	钢板3	ø100×6	Q235	4	0.4	1.6

说明：

1.除非另有说明，所有材料均为Q235钢。

2.除非另有说明，所有圆角半径均为R25。

中交二公局工程设计研究院	张靖皋长江大桥施工暨股权投资项目 ZJG-A7标段	猫道门架（2）	设计		复核		一审		二审		三审		图号	MD4-03	日期	2025.08