中间模块立面桁架片

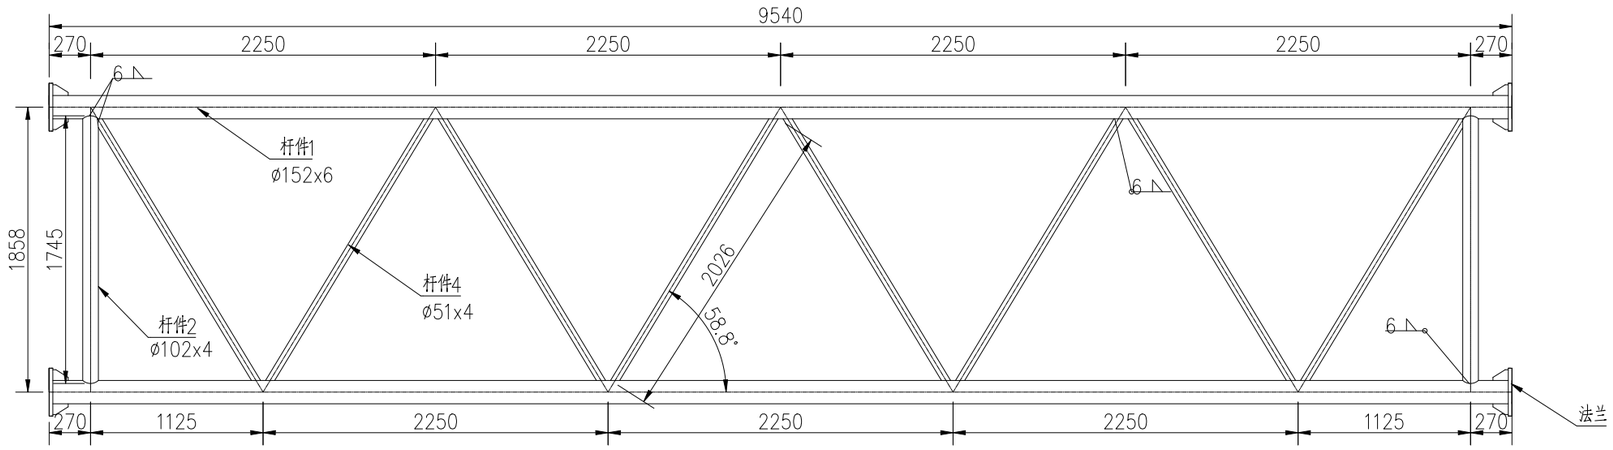

桁架横断面图

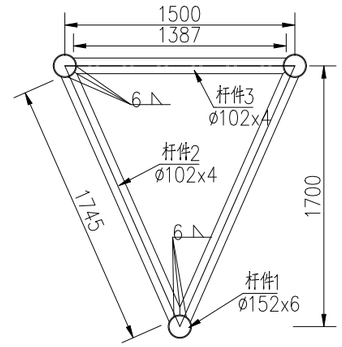

中间模块顶面桁架片

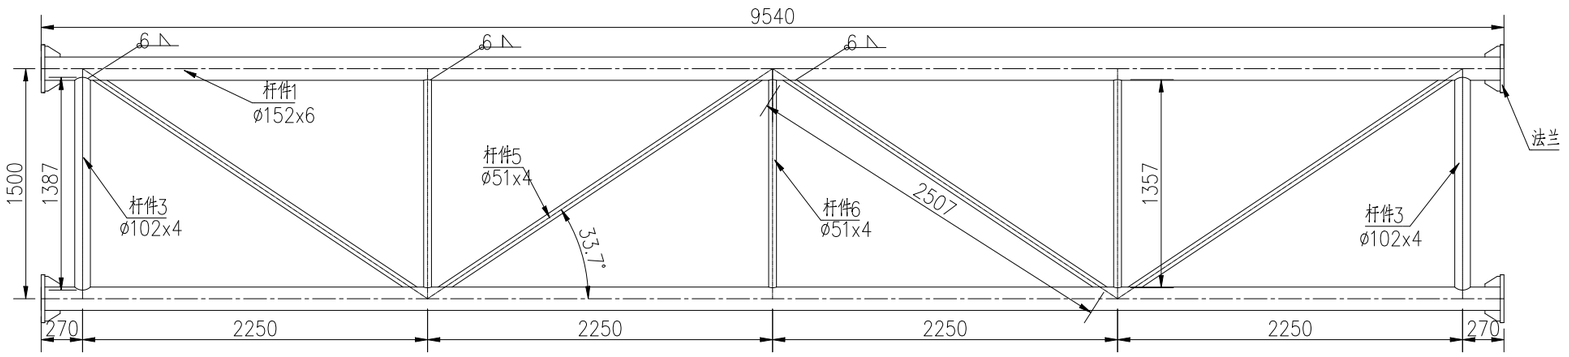

说明：1、本图尺寸除特殊说明外，其余均以mm计；
2、图中未标出类型焊缝焊脚高度均为6mm。

中交二公局工程设计研究院	张靖皋长江大桥施工暨股权投资项目 ZJG-A7标段	横向通道中间模块桁架结构图	设计		复核		一审		二审		三审		图号	MD5-04	日期	2025.08