



横向通道立面图

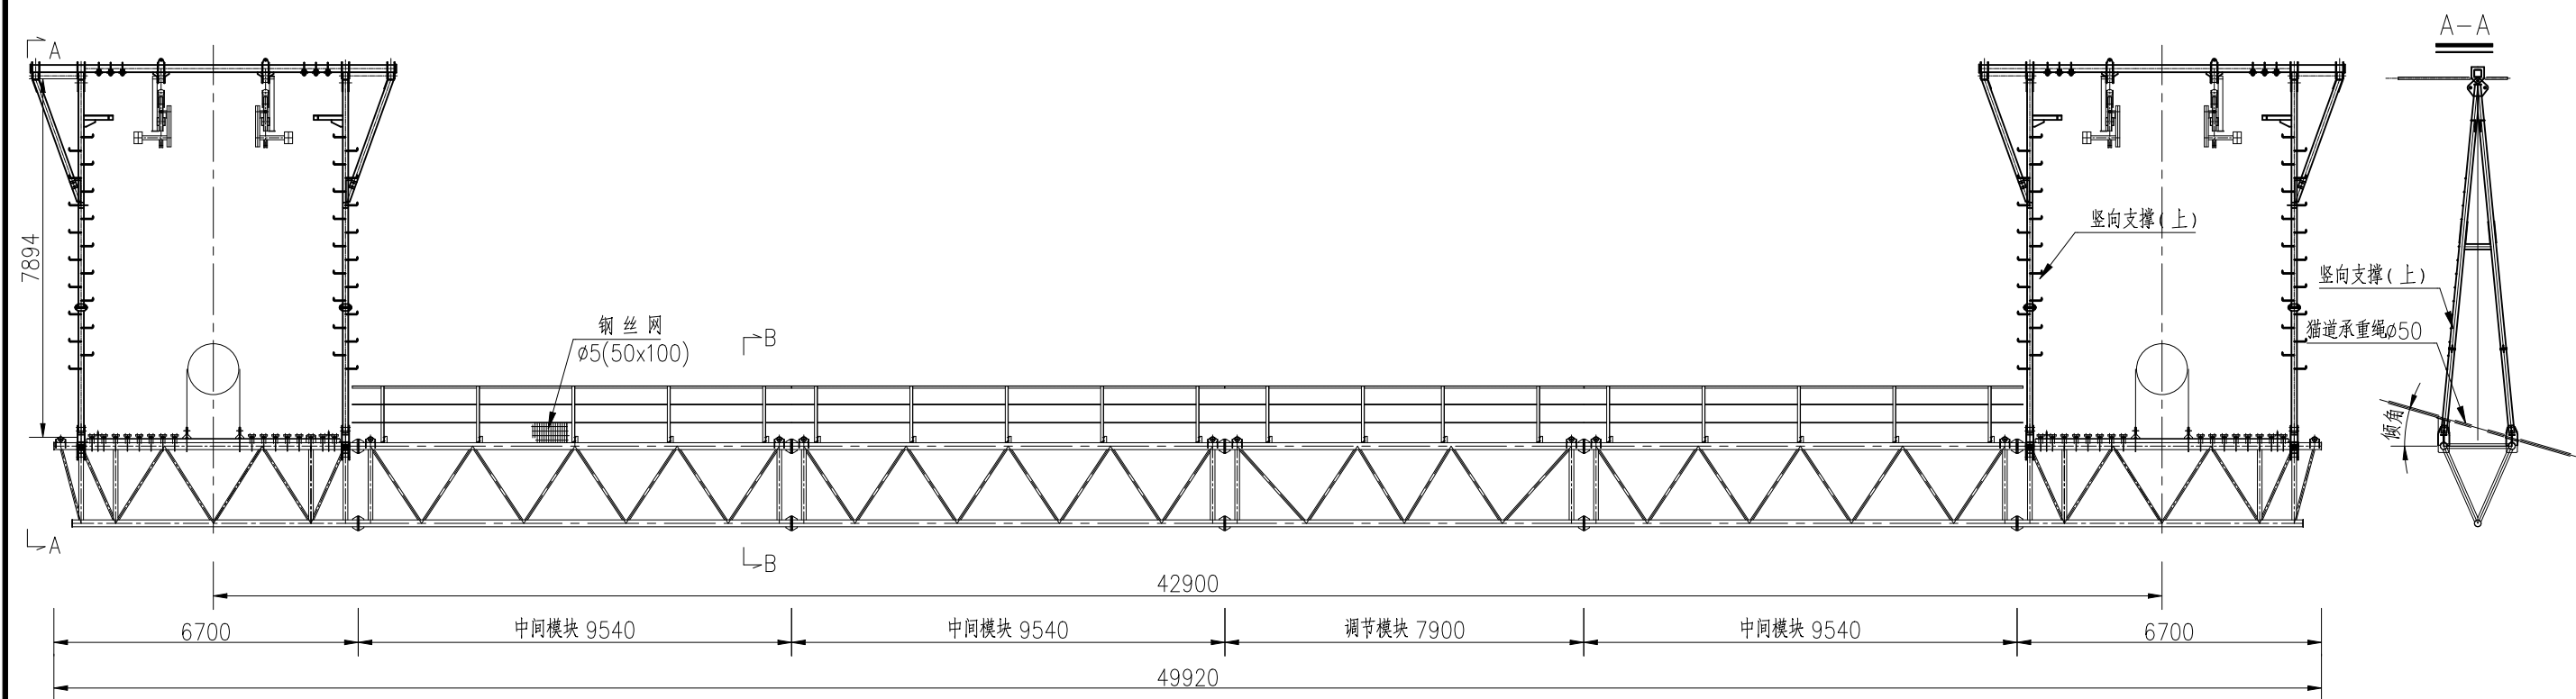

横向通道平面图

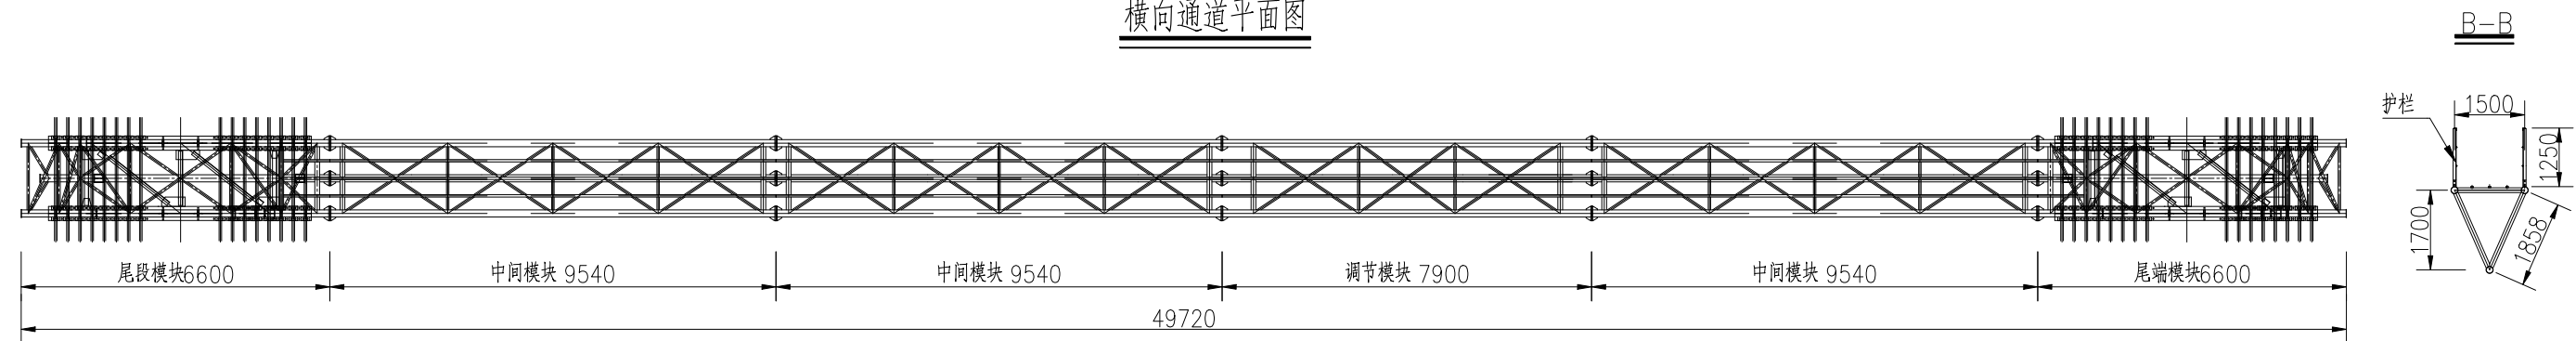

横向通道支架与承重索夹角

| 通道编号 | 夹角(°) | 通道编号 | 夹角(°)  | 通道编号 | 夹角(°)  |
|------|-------|------|--------|------|--------|
| H1   | 0     | H5   | 12.44  | H9   | 163.01 |
| H2   | 2.82  | H6   | 15.68  | H10  | 166.64 |
| H3   | 5.63  | H7   | 18.89  | H11  | 169.22 |
| H4   | 8.75  | H8   | 159.76 | H12  | 172.61 |

说明：

1. 本图尺寸除特殊说明外，其余均以mm计；
2. 各部分具体尺寸见相关图纸。
3. 本桥猫道横向通道共投入12道。