


中间模块立面图

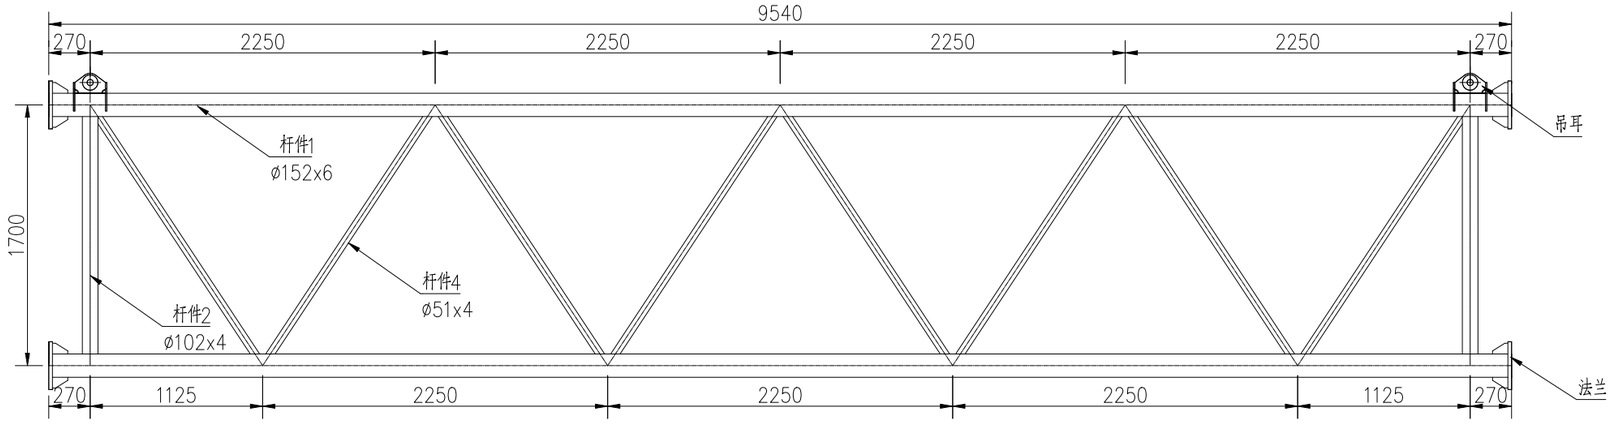

中间模块侧面图

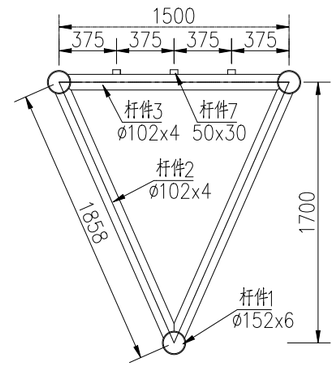

中间模块平面图

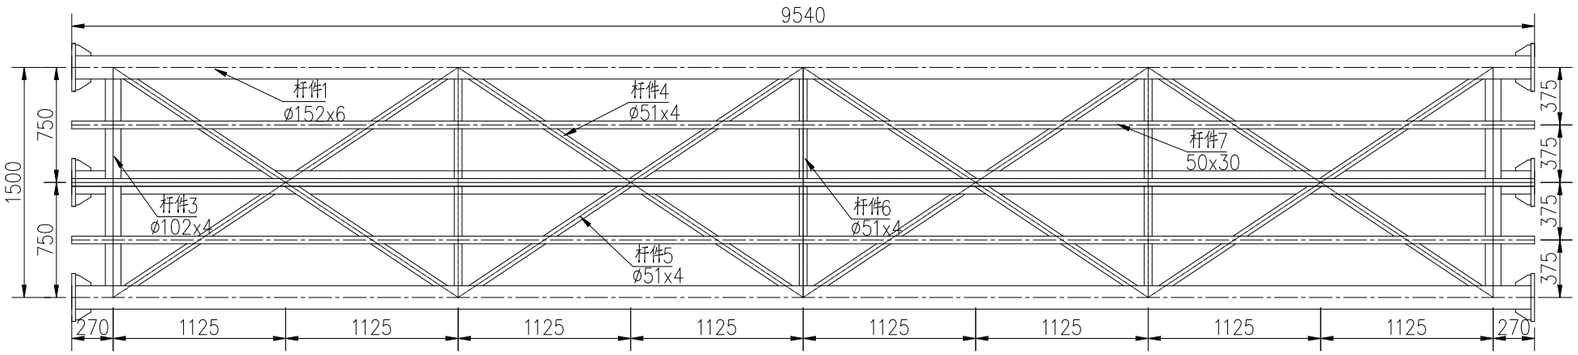

中间模块材料数量表（单个通道共3套）

序号	名称	型号	材质	单根长度（mm）	数量	单位重量（kg/m）	总重（kg）
1	杆件1	ø152x6	Q235	9540	3	21.6	618.2
2	杆件2	ø102x4	Q235	1745	4	9.7	67.7
3	杆件3	ø102x4	Q235	1387	2	9.7	26.9
4	杆件4	ø51x4	Q235	2026	16	4.6	149.1
5	杆件5	ø51x4	Q235	2507	4	4.6	46.1
6	杆件6	ø51x4	Q235	1357	3	4.6	18.7
7	杆件7	50x30x4	Q235	9540	3	4.5	128.8
合计							1055.5
此外包括模块吊耳4个，法兰6个。							

说明：

1、本图尺寸除特殊说明外，其余均以mm计；

2.本标段猫道横向通道共投入12道。

3.横向通道下滑导轮采用猫道门架下滑导轮，故不再做设计加工。

中交二公局工程设计研究院	张靖皋长江大桥施工暨股权投资项目 ZJG-A7标段	横向通道中间模块总体图	设计		复核		一审		二审		三审		图号	MD5-03	日期	2025.08