



猫道门架(1)

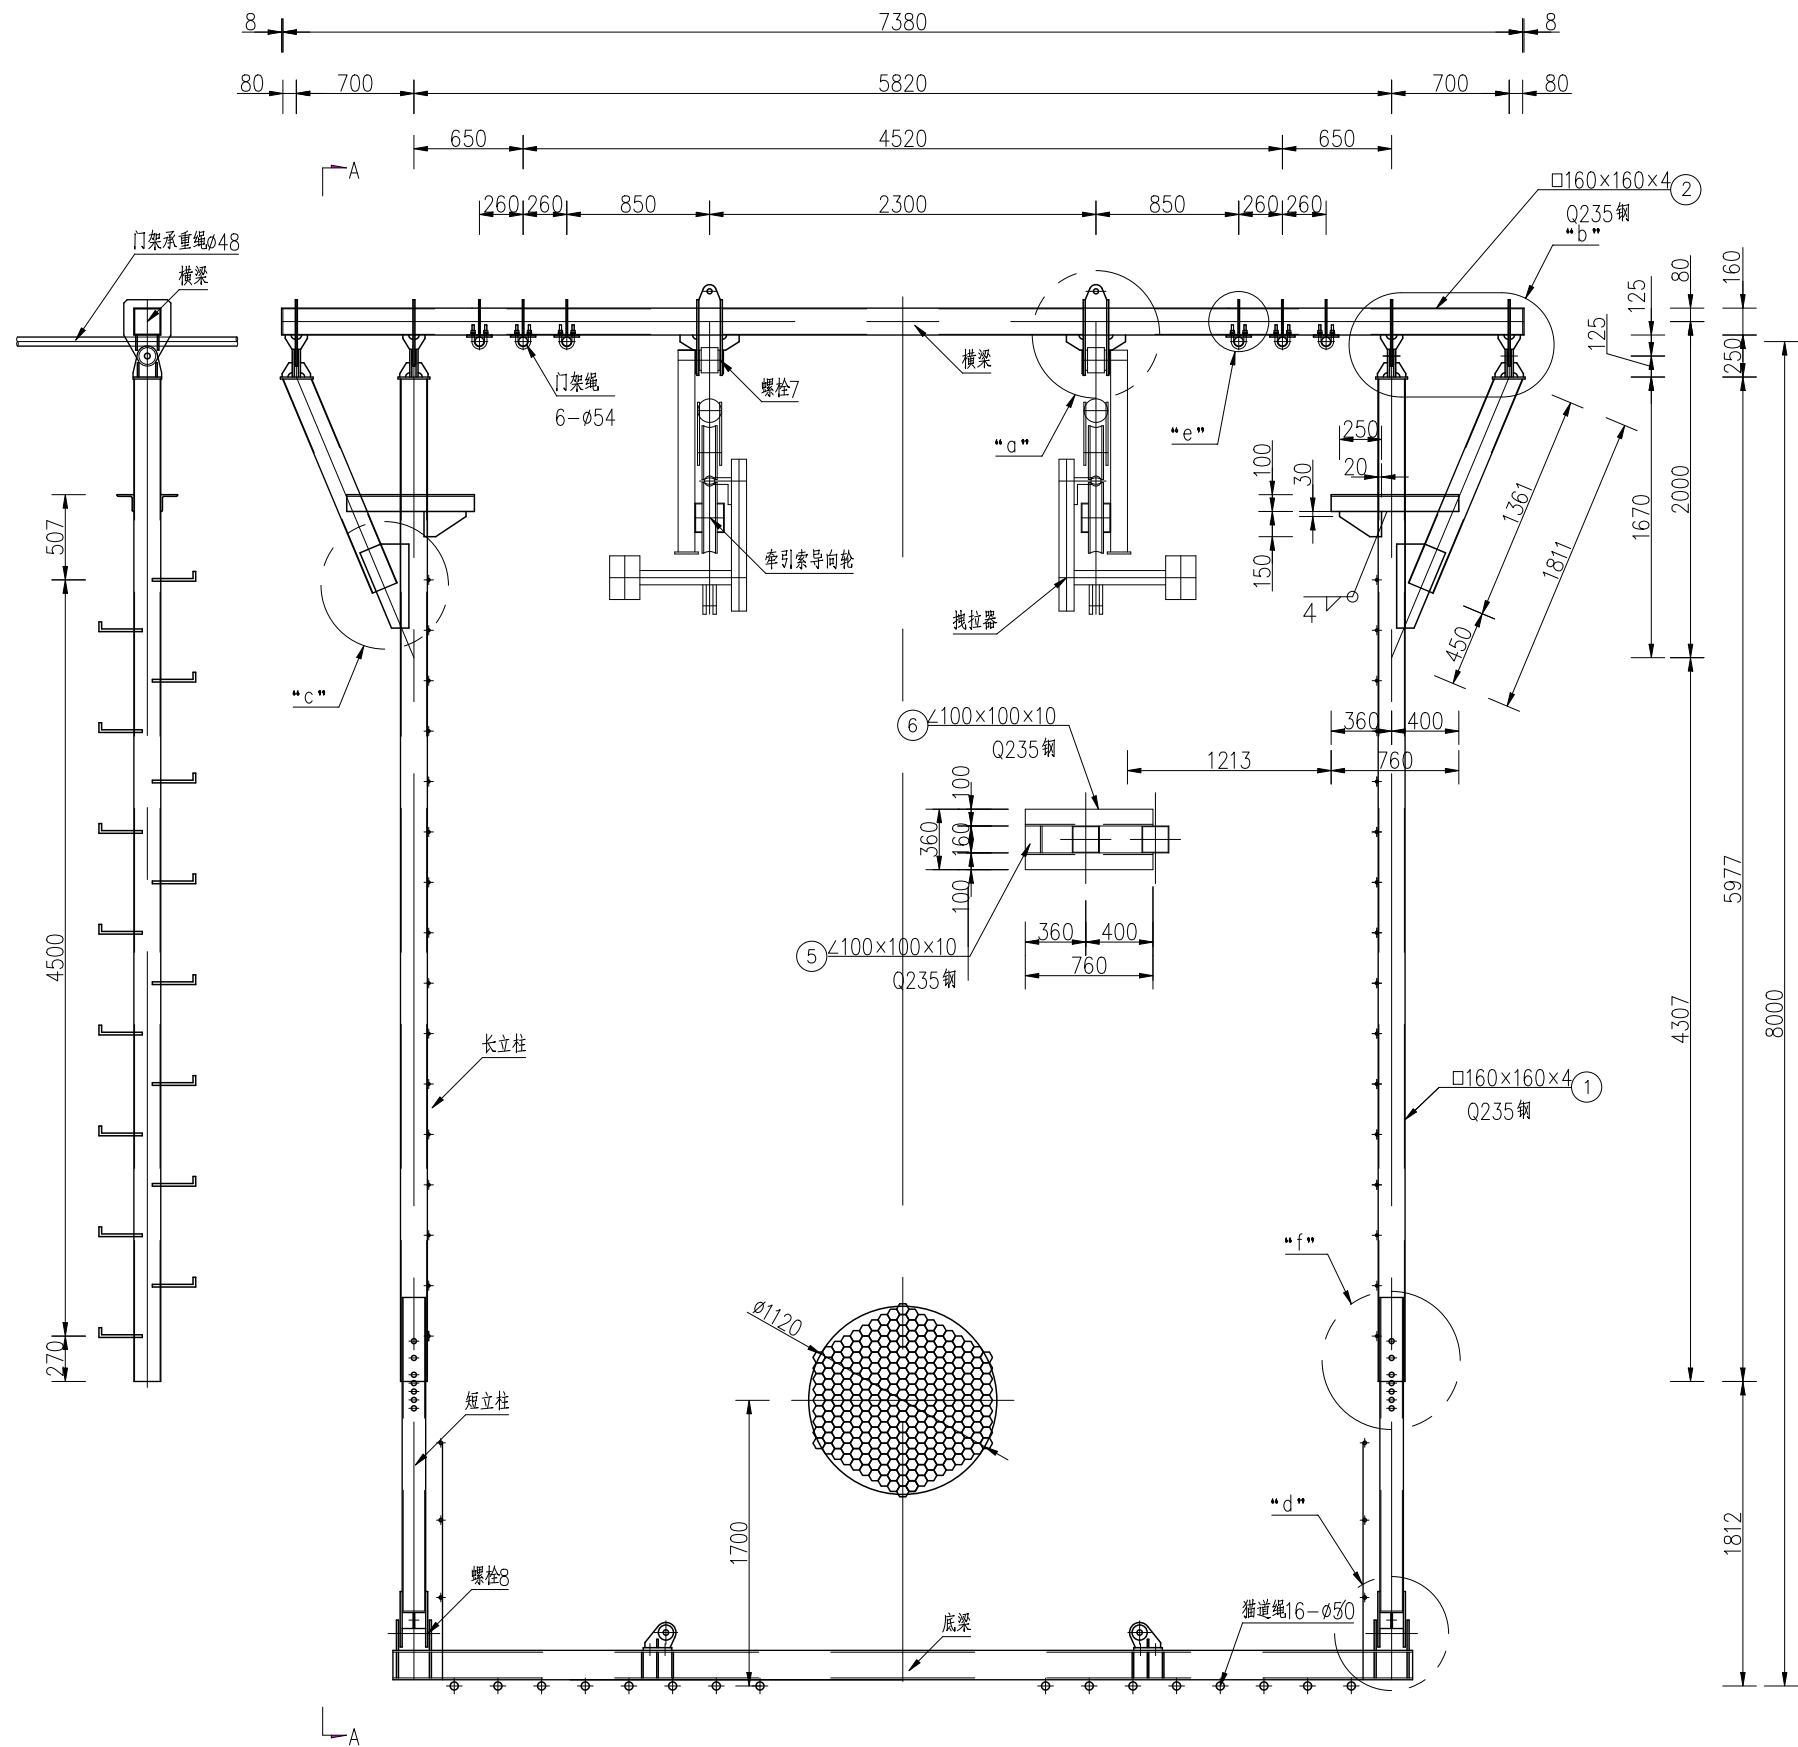

“C大样”

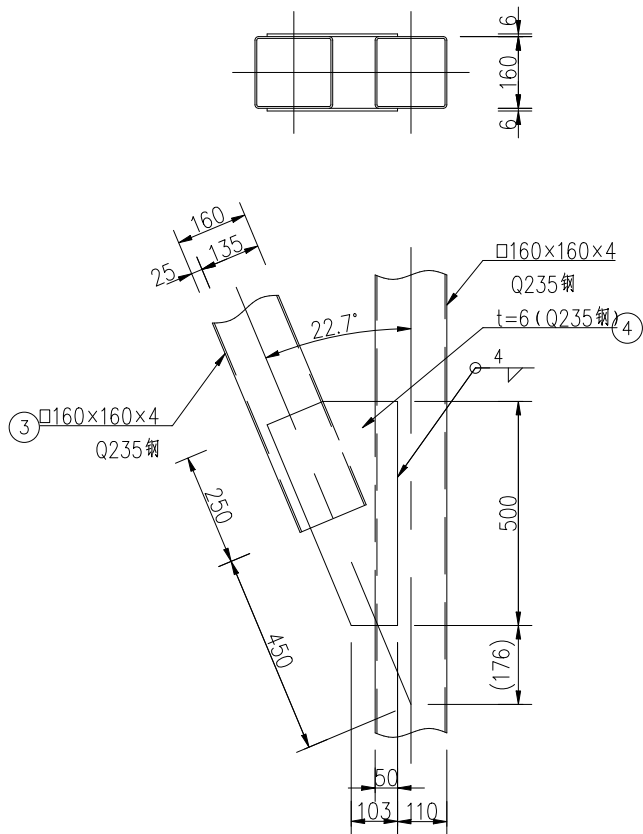

单套材料数量表 (单幅共71套)

编号	名称	规格	材质	数量	单重	合计
1	方钢管1	□160×160×4×5965	Q235	2	101.5	203.0
2	方钢管2	□160×160×4×7380	Q235	1	115.6	115.6
3	方钢管3	□160×160×4×1382	Q235	2	20.1	40.1
4	钢板	500×291×6	Q235	4	6.9	27.4
5	型钢1	∠100×100×10×160	Q235	2	2.4	4.8
6	型钢2	∠100×100×10×760	Q235	4	16.6	66.4
7	肋板	250×150×6	Q235	4	1.8	7.1
8	圆钢	φ16×300	Q235	28	0.5	13.2

说明:

1. 所有材料均为Q235钢。
2. 所有圆角半径均为R25。