



横向通道立面图

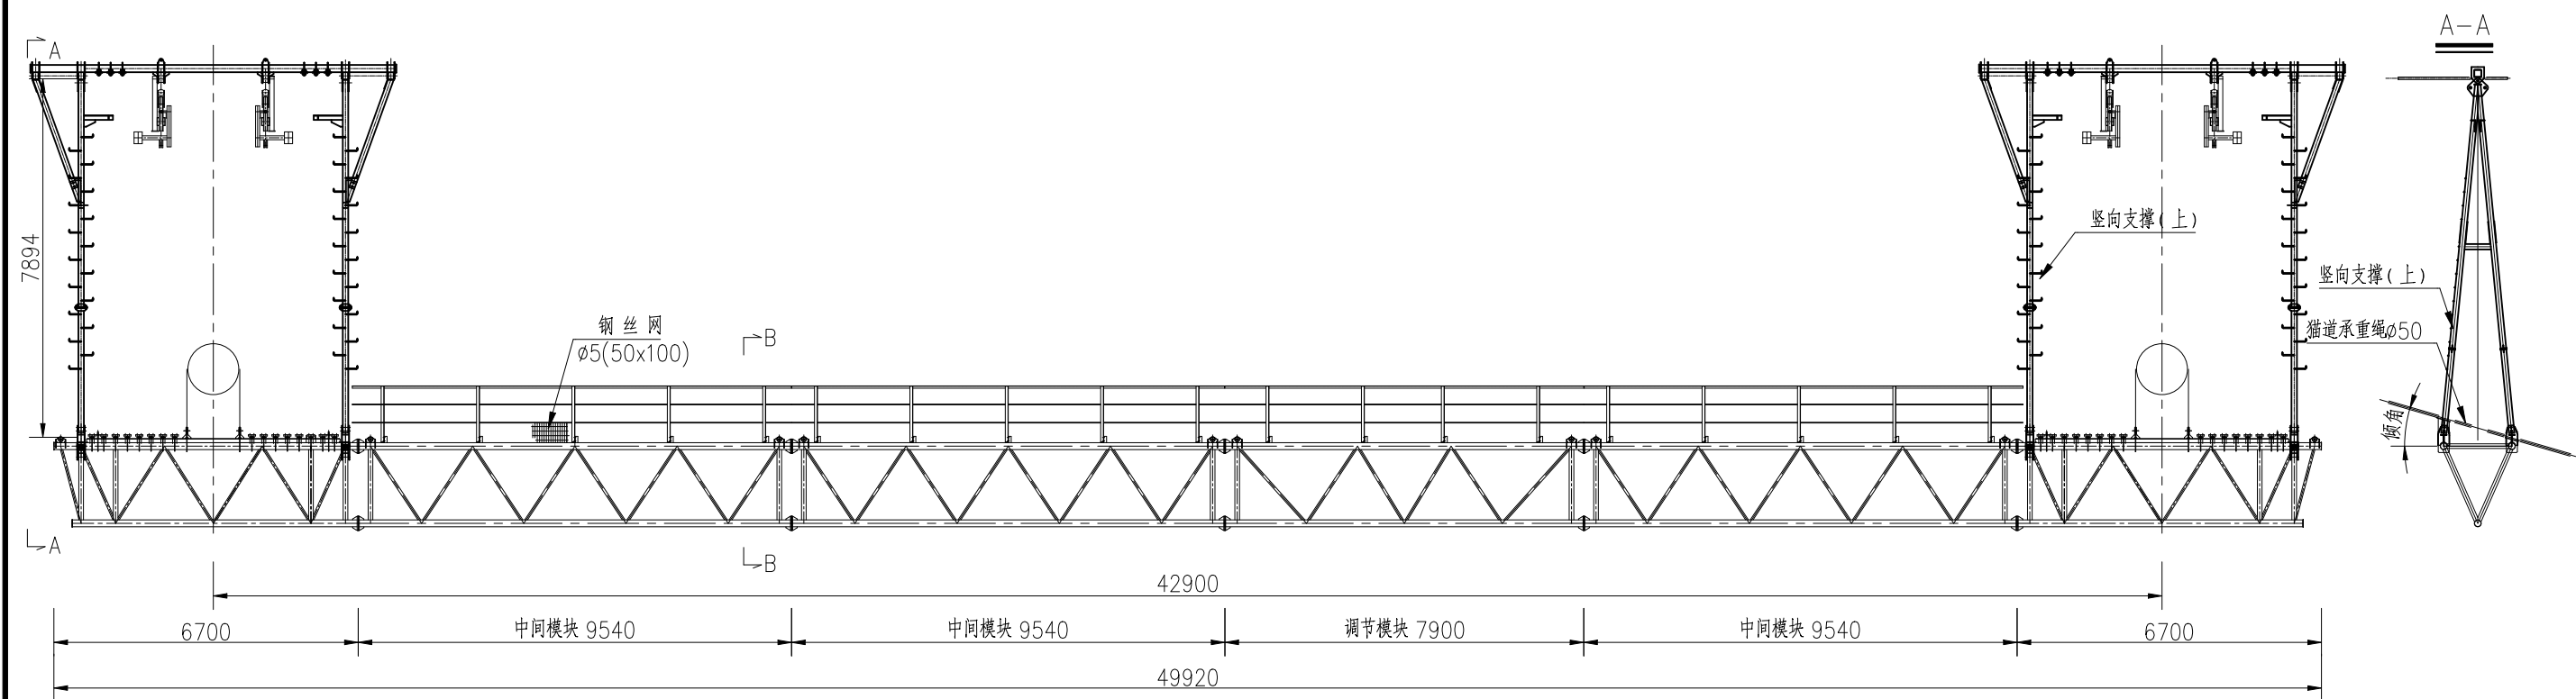

横向通道平面图

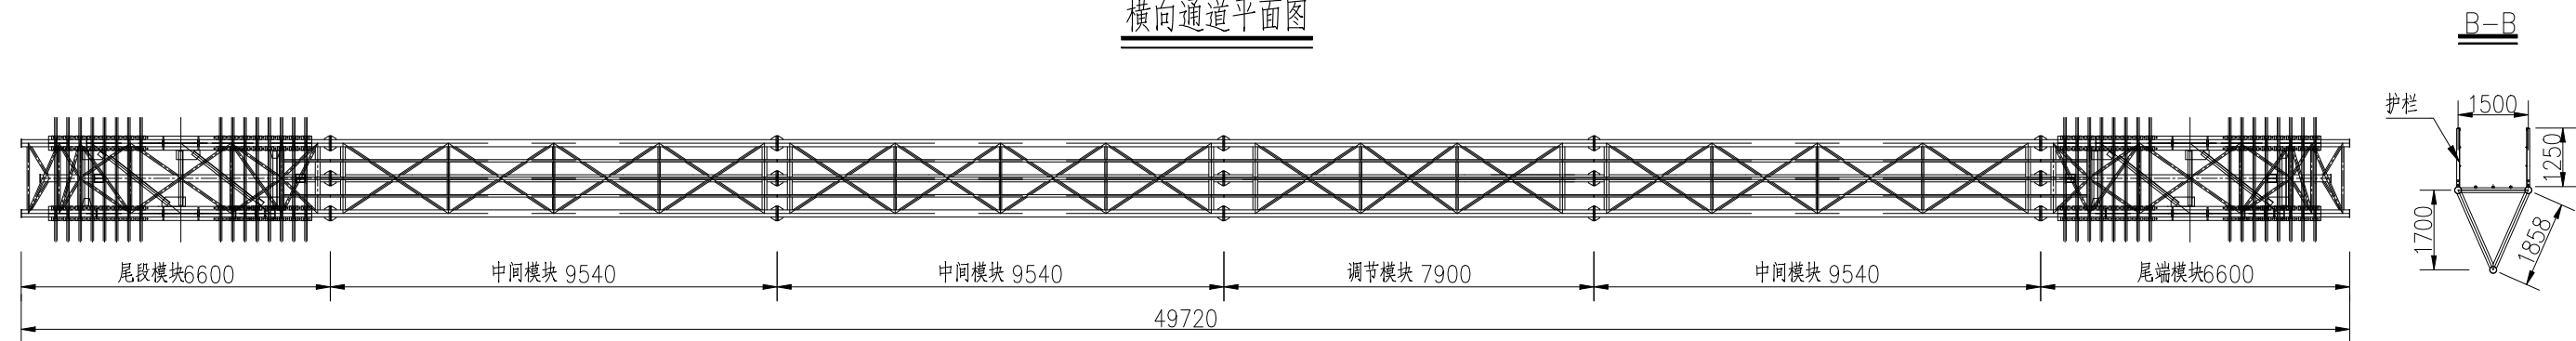

横向通道支架与承重索夹角

通道编号	夹角($^{\circ}$)	通道编号	夹角($^{\circ}$)	通道编号	夹角($^{\circ}$)
H1	0	H5	12.44	H9	163.01
H2	2.82	H6	15.68	H10	166.64
H3	5.63	H7	18.89	H11	169.22
H4	8.75	H8	159.76	H12	172.61

说明：

1. 本图尺寸除特殊说明外，其余均以mm计；
2. 各部分具体尺寸见相关图纸。
3. 本桥猫道横向通道共投入12道。